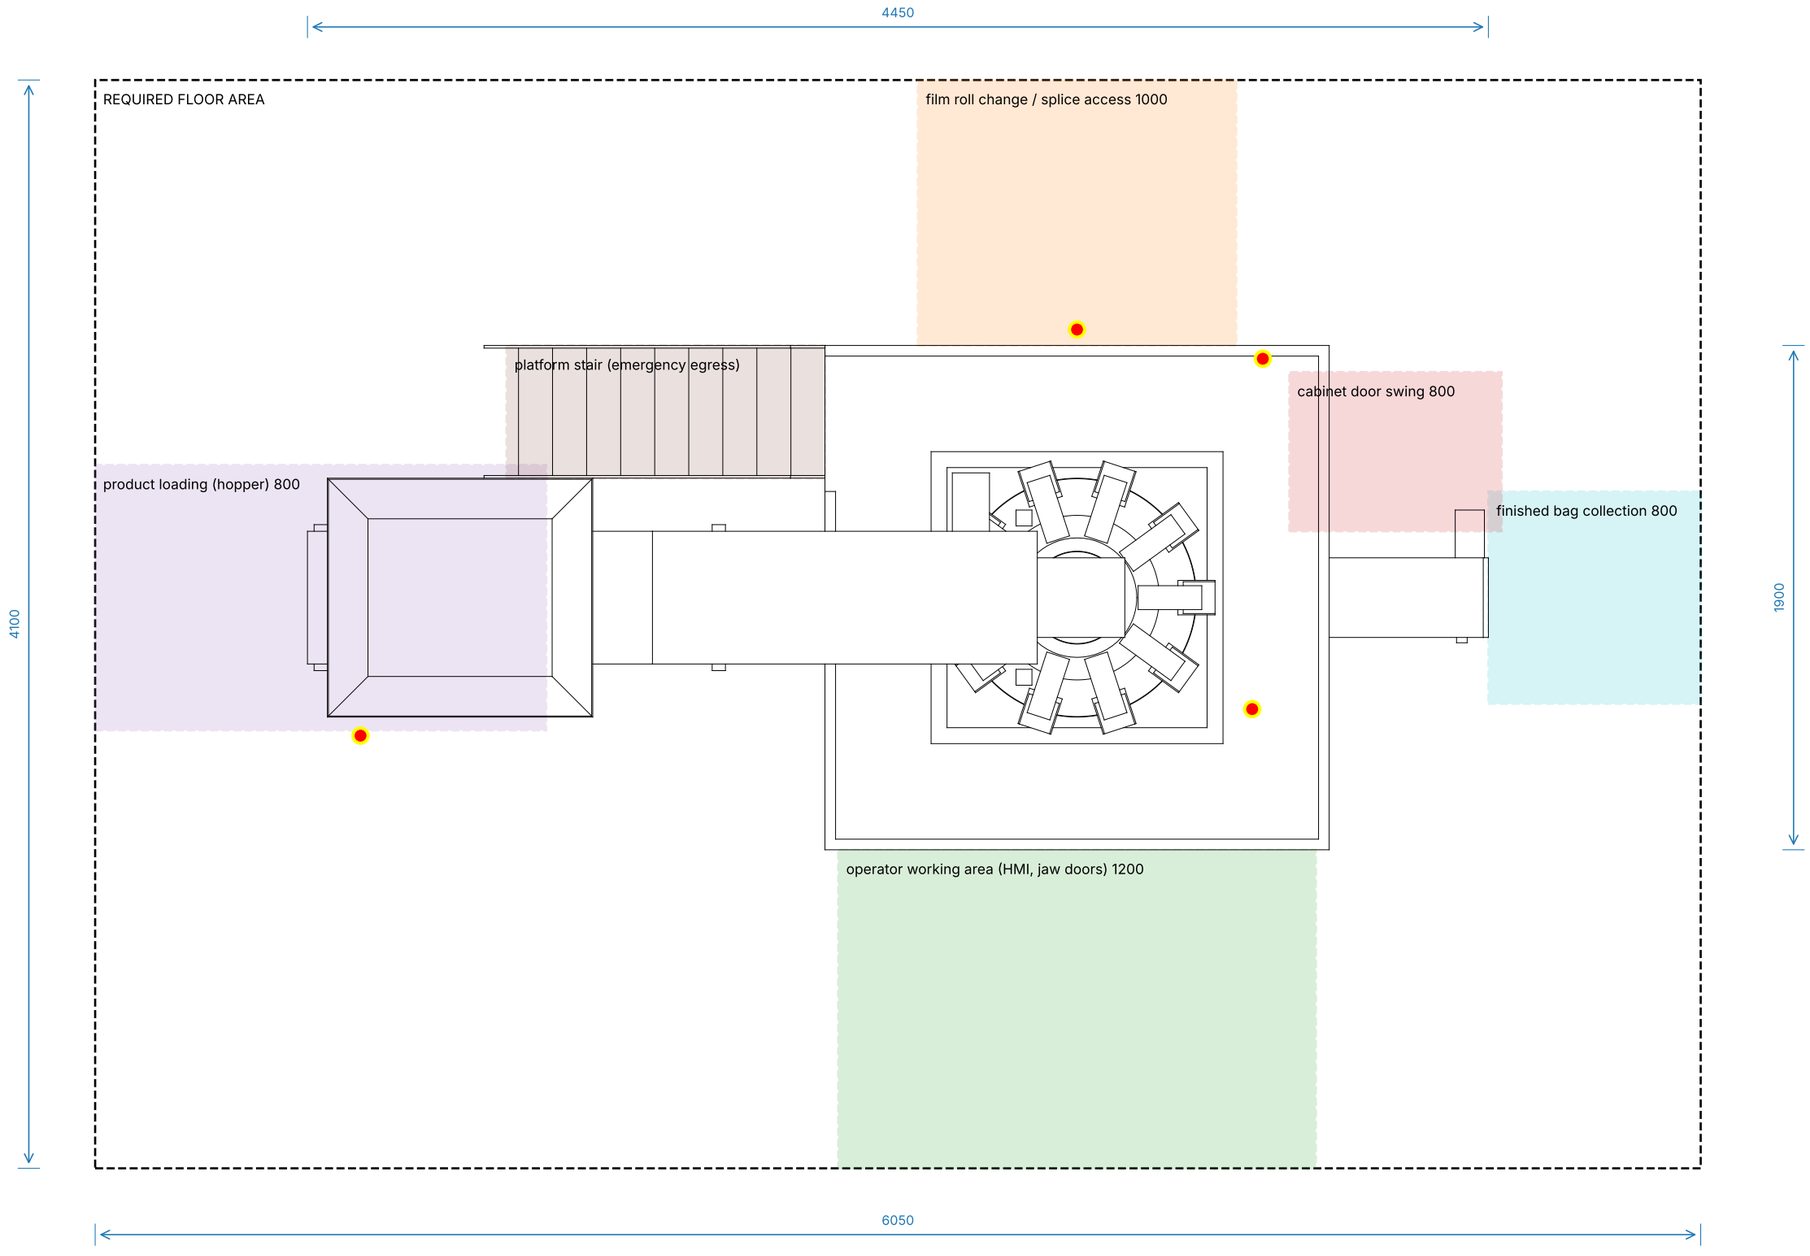FLOOR LAYOUT required area 6050 × 4100 mm = 24.8 m2, min. clear ceiling 4400 mm. Emergency stops: HMI station, rear film side, platform, elevator infeed.